
ANEXO ÚNICO

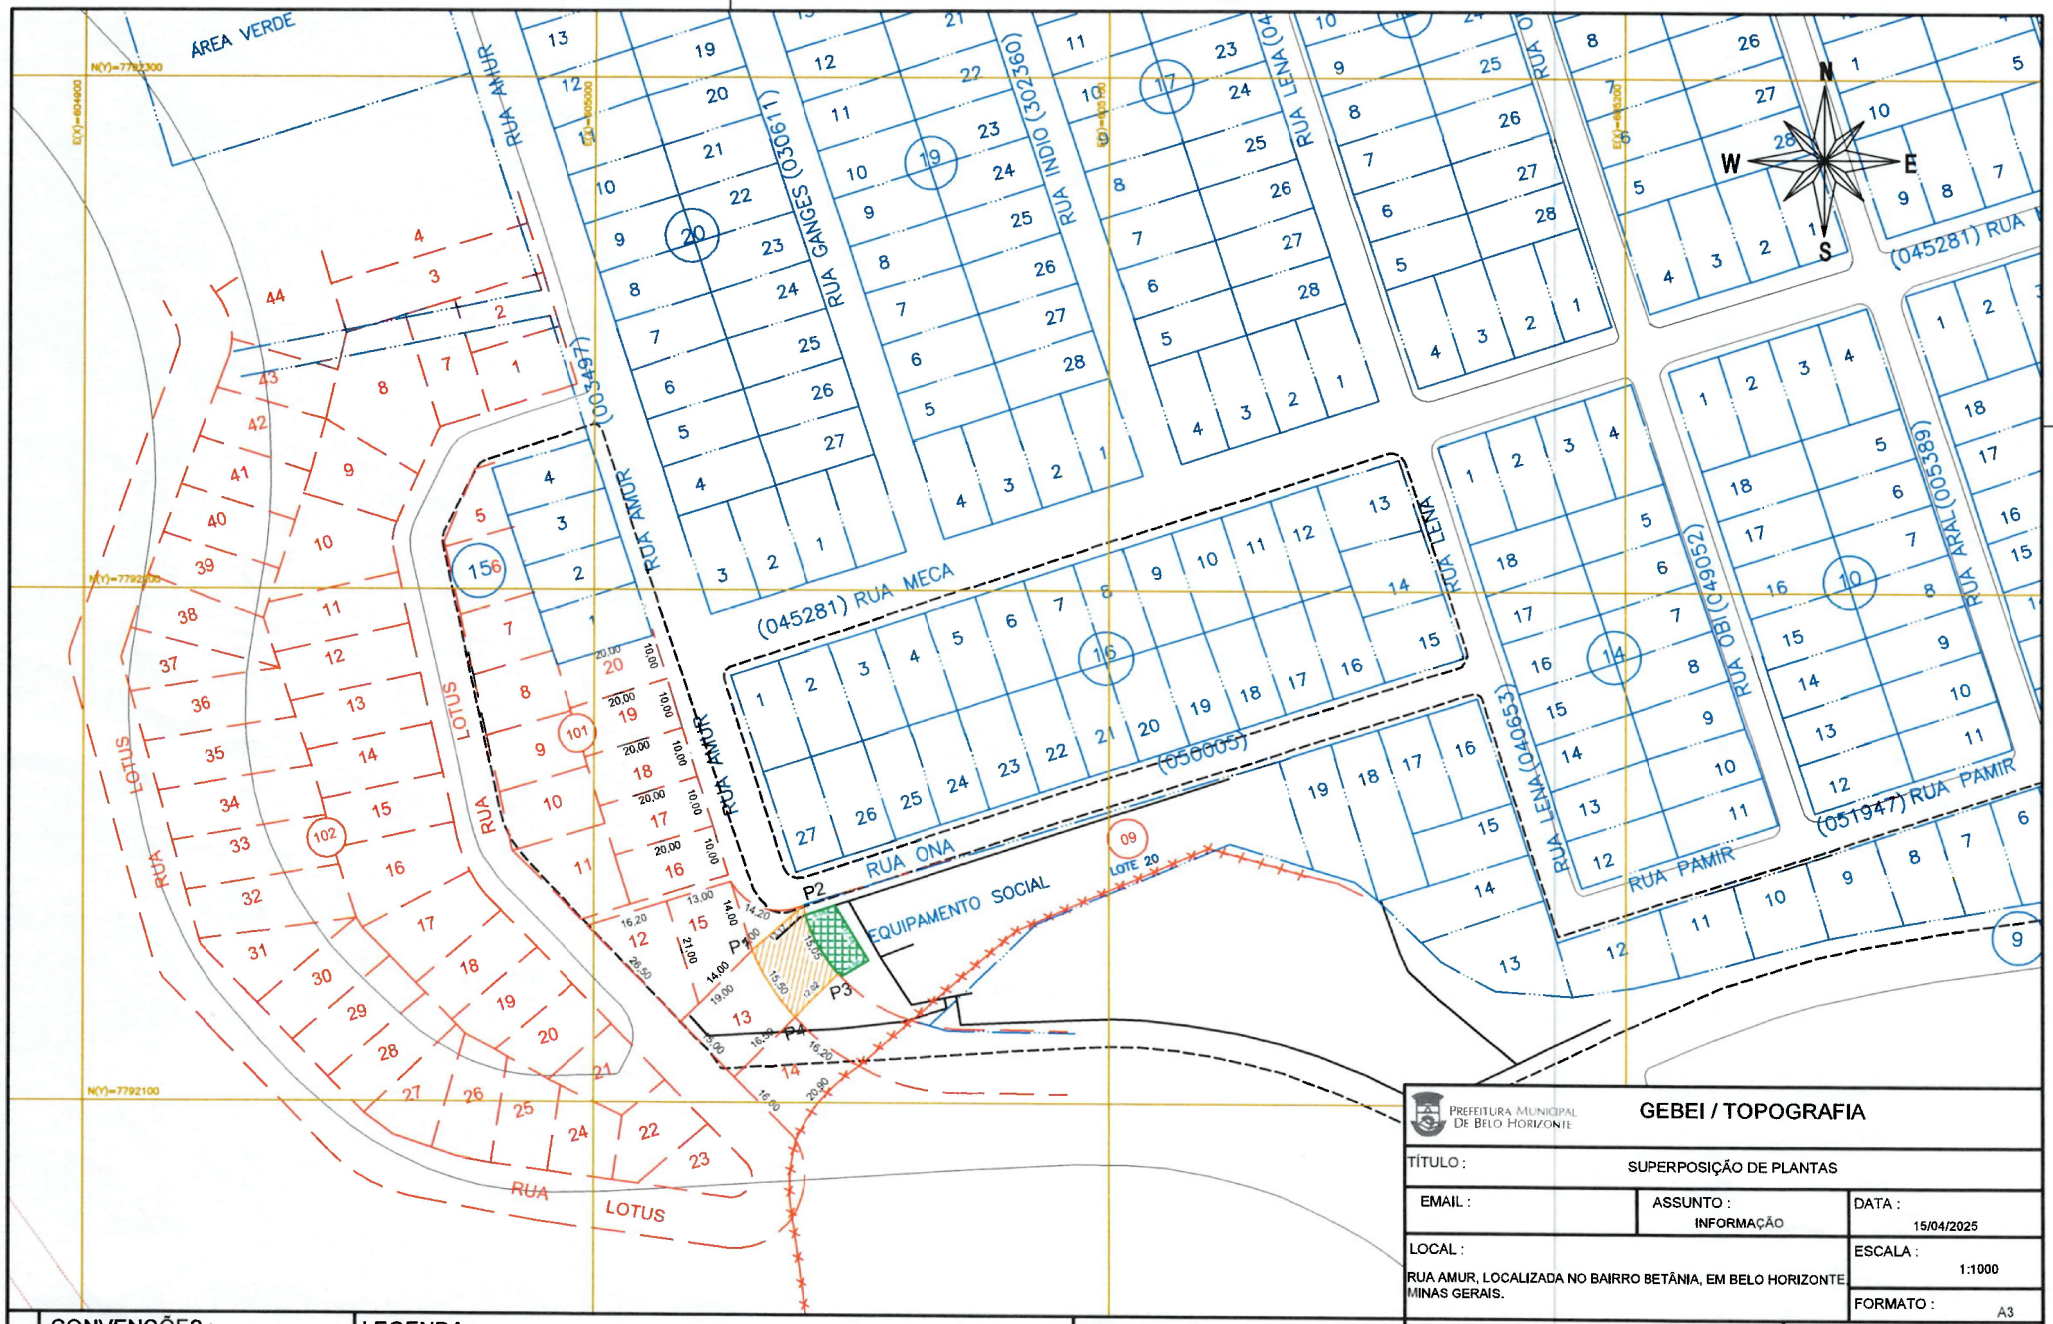

NOTAS

CONVENÇÕES :

- CP-217-001-H / (CONJUNTO HABITACIONAL BETÂNIA)
- PLANTA PARTICULAR VILA BETÂNIA
- CERCA

LEGENDA :

ÁREA OCUPADA REFERENTE AO TRECHO NÃO IMPLANTADO DA RUA AMUR APROVADA PELO CP.217-001-H = 183.20 m²

ÁREA OCUPADA REFERENTE A PARTE DO LOTE 20 DO QUARTEIRÃO 09 DESTINADA A EQUIPAMENTO SOCIAL. CONFORME CP.217-001-H = 86,66m².

ASSUNTO :

LEVANTAMENTO TOPOGRÁFICO DO TRECHO NÃO IMPLANTADO DA RUA AMUR, SITUADO ENTRE O LOTE 13 DO QUARTEIRÃO 101 DA VILA BETÂNIA -PLANTA PARTICULAR - E LOTE 20 DO QUARTEIRÃO 09 - EQUIPAMENTO SOCIAL- DO CONJUNTO HABITACIONAL BETÂNIA CP-217-001-H.

PREFEITURA MUNICIPAL DE BELO HORIZONTE

GEBEI / TOPOGRAFIA

TÍTULO : SUPERPOSIÇÃO DE PLANTAS		
EMAIL :	ASSUNTO : INFORMAÇÃO	DATA : 15/04/2025
LOCAL : RUA AMUR, LOCALIZADA NO BAIRRO BETÂNIA, EM BELO HORIZONTE. MINAS GERAIS.		ESCALA : 1:1000
		FORMATO : A3
RESP. TÉCNICO : CLÁUDIO ADRIANO GALDINO – CREA - 52002/D-MG		GEBEI / TOPOGRAFIA : VALDIR SOARES THOMAZ BM: 30127
DESENHISTA : MARCOS CALAZANS C		